



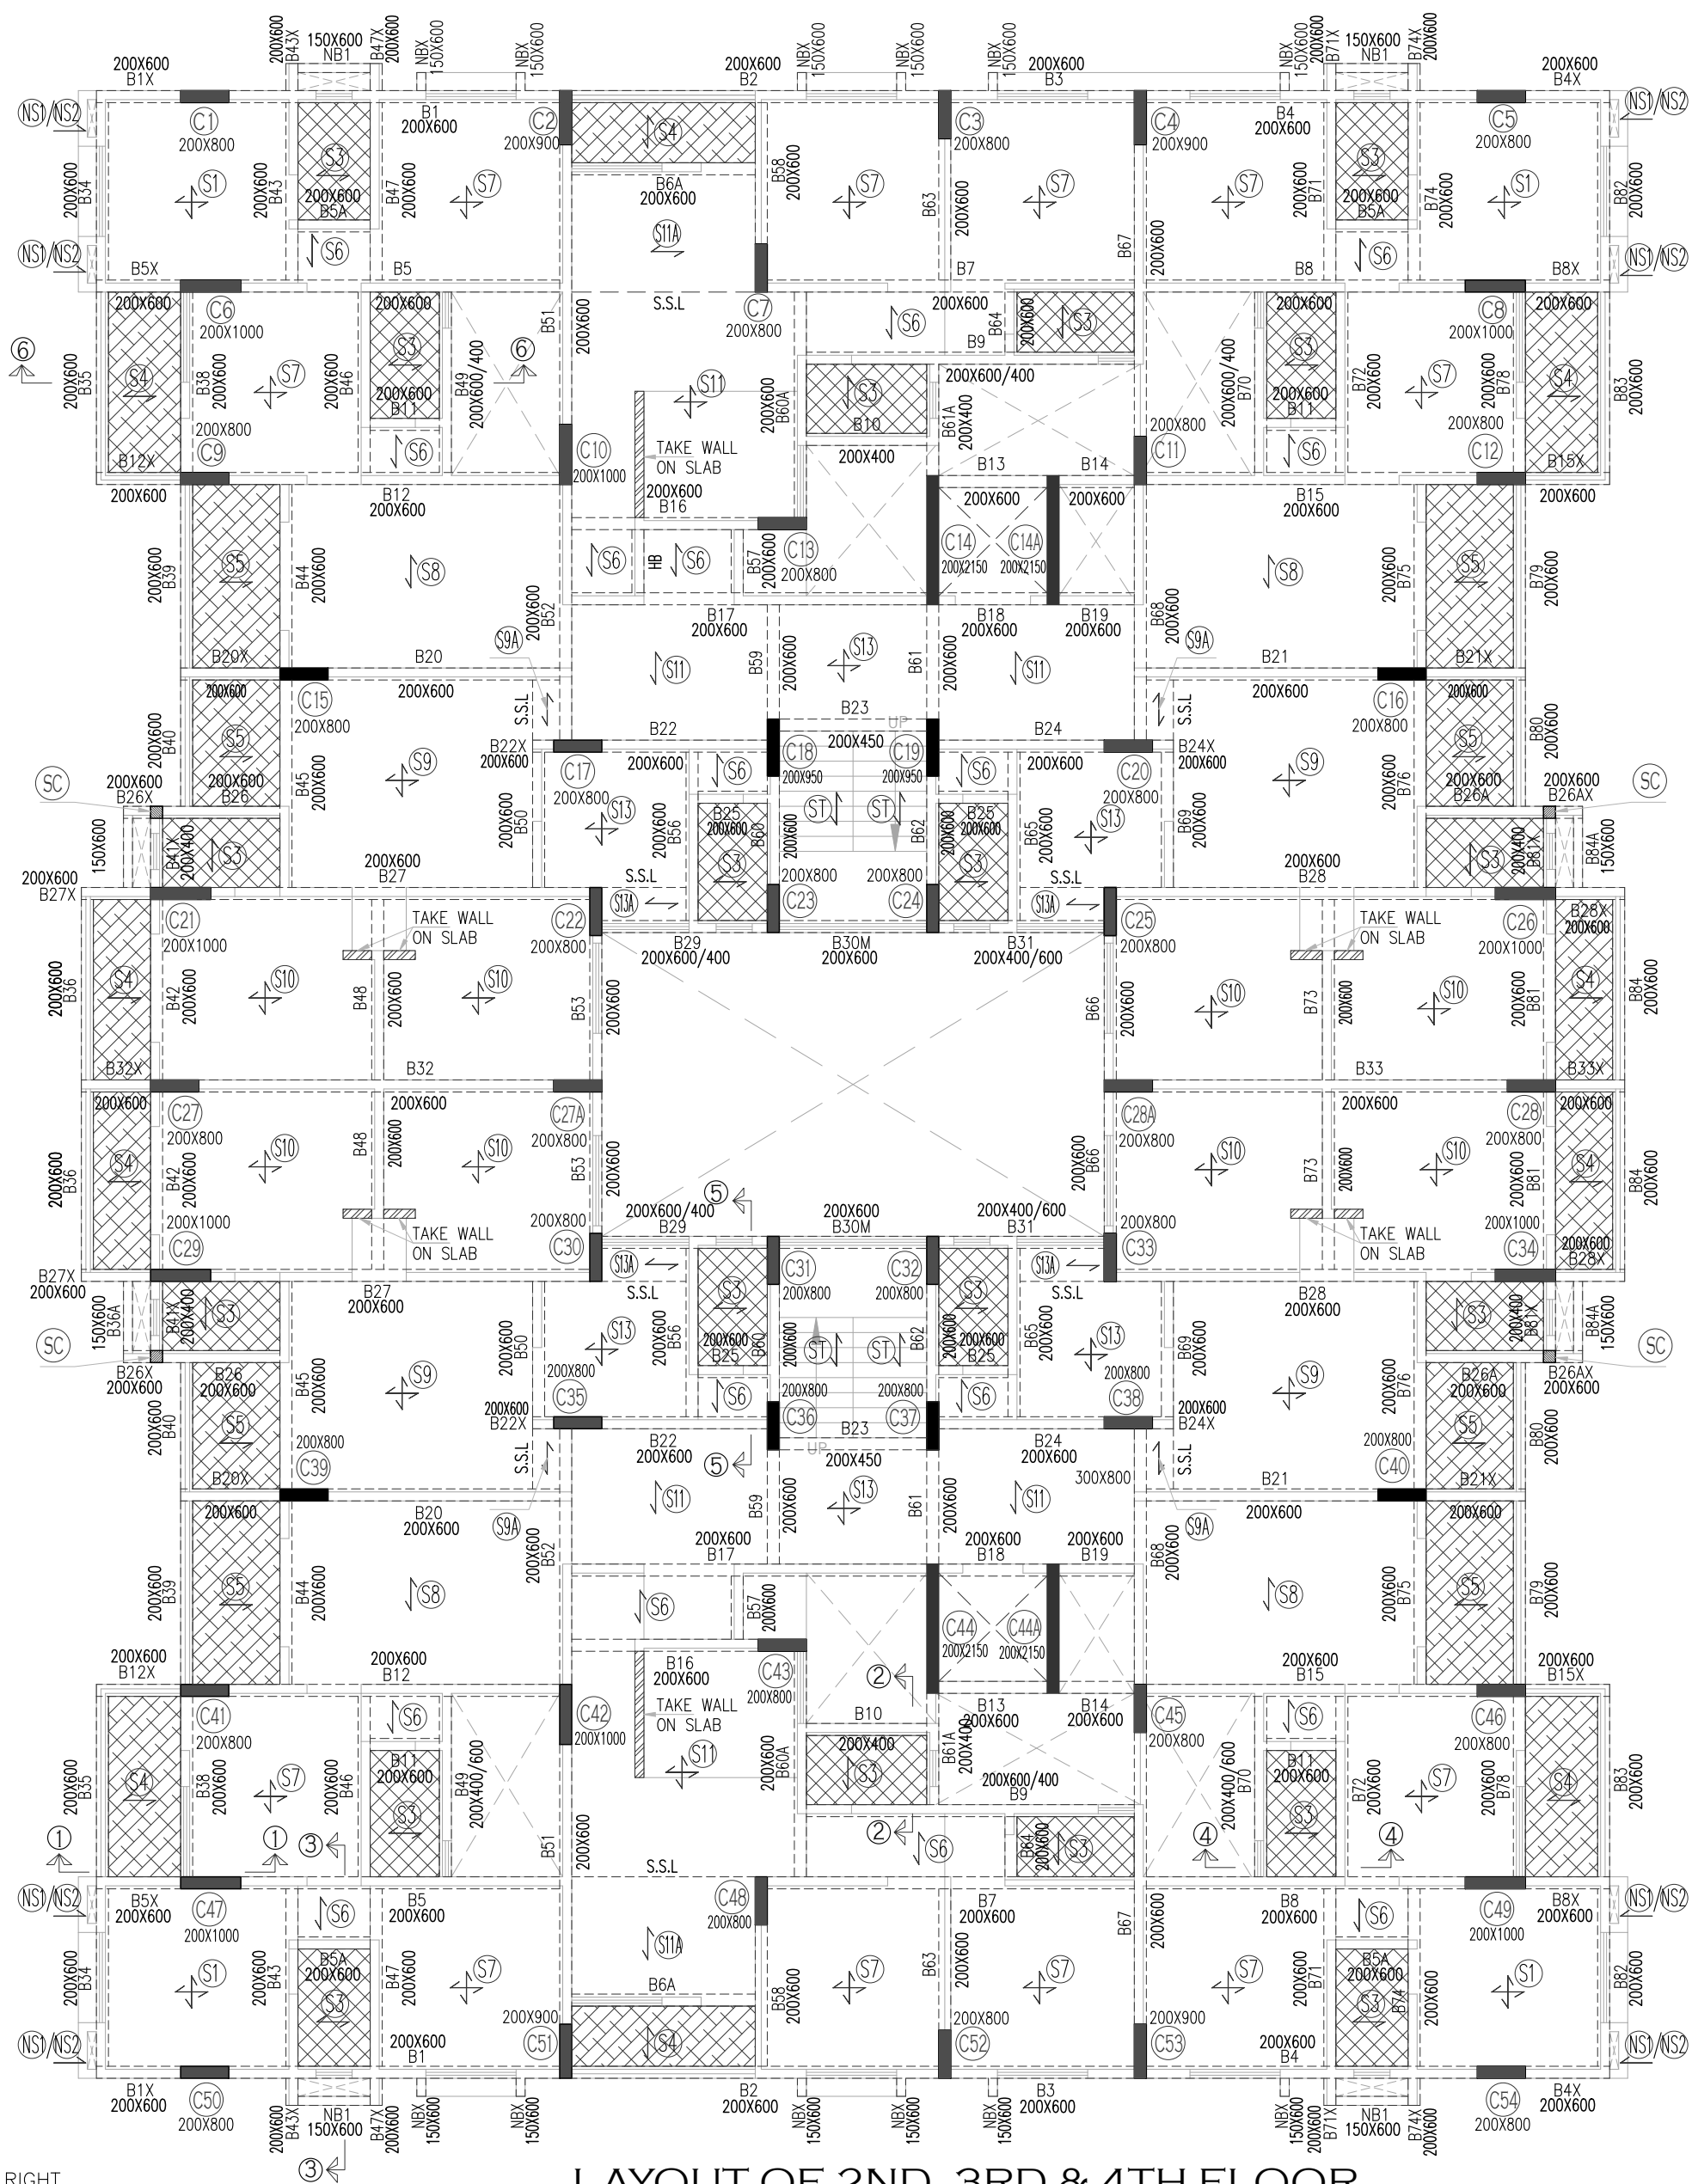

LAYOUT OF 2ND, 3RD & 4TH FLOOR
BUILDING-B

LEFT RIGHT
DIRECTIONS FOR
EXTRA TOP STEEL

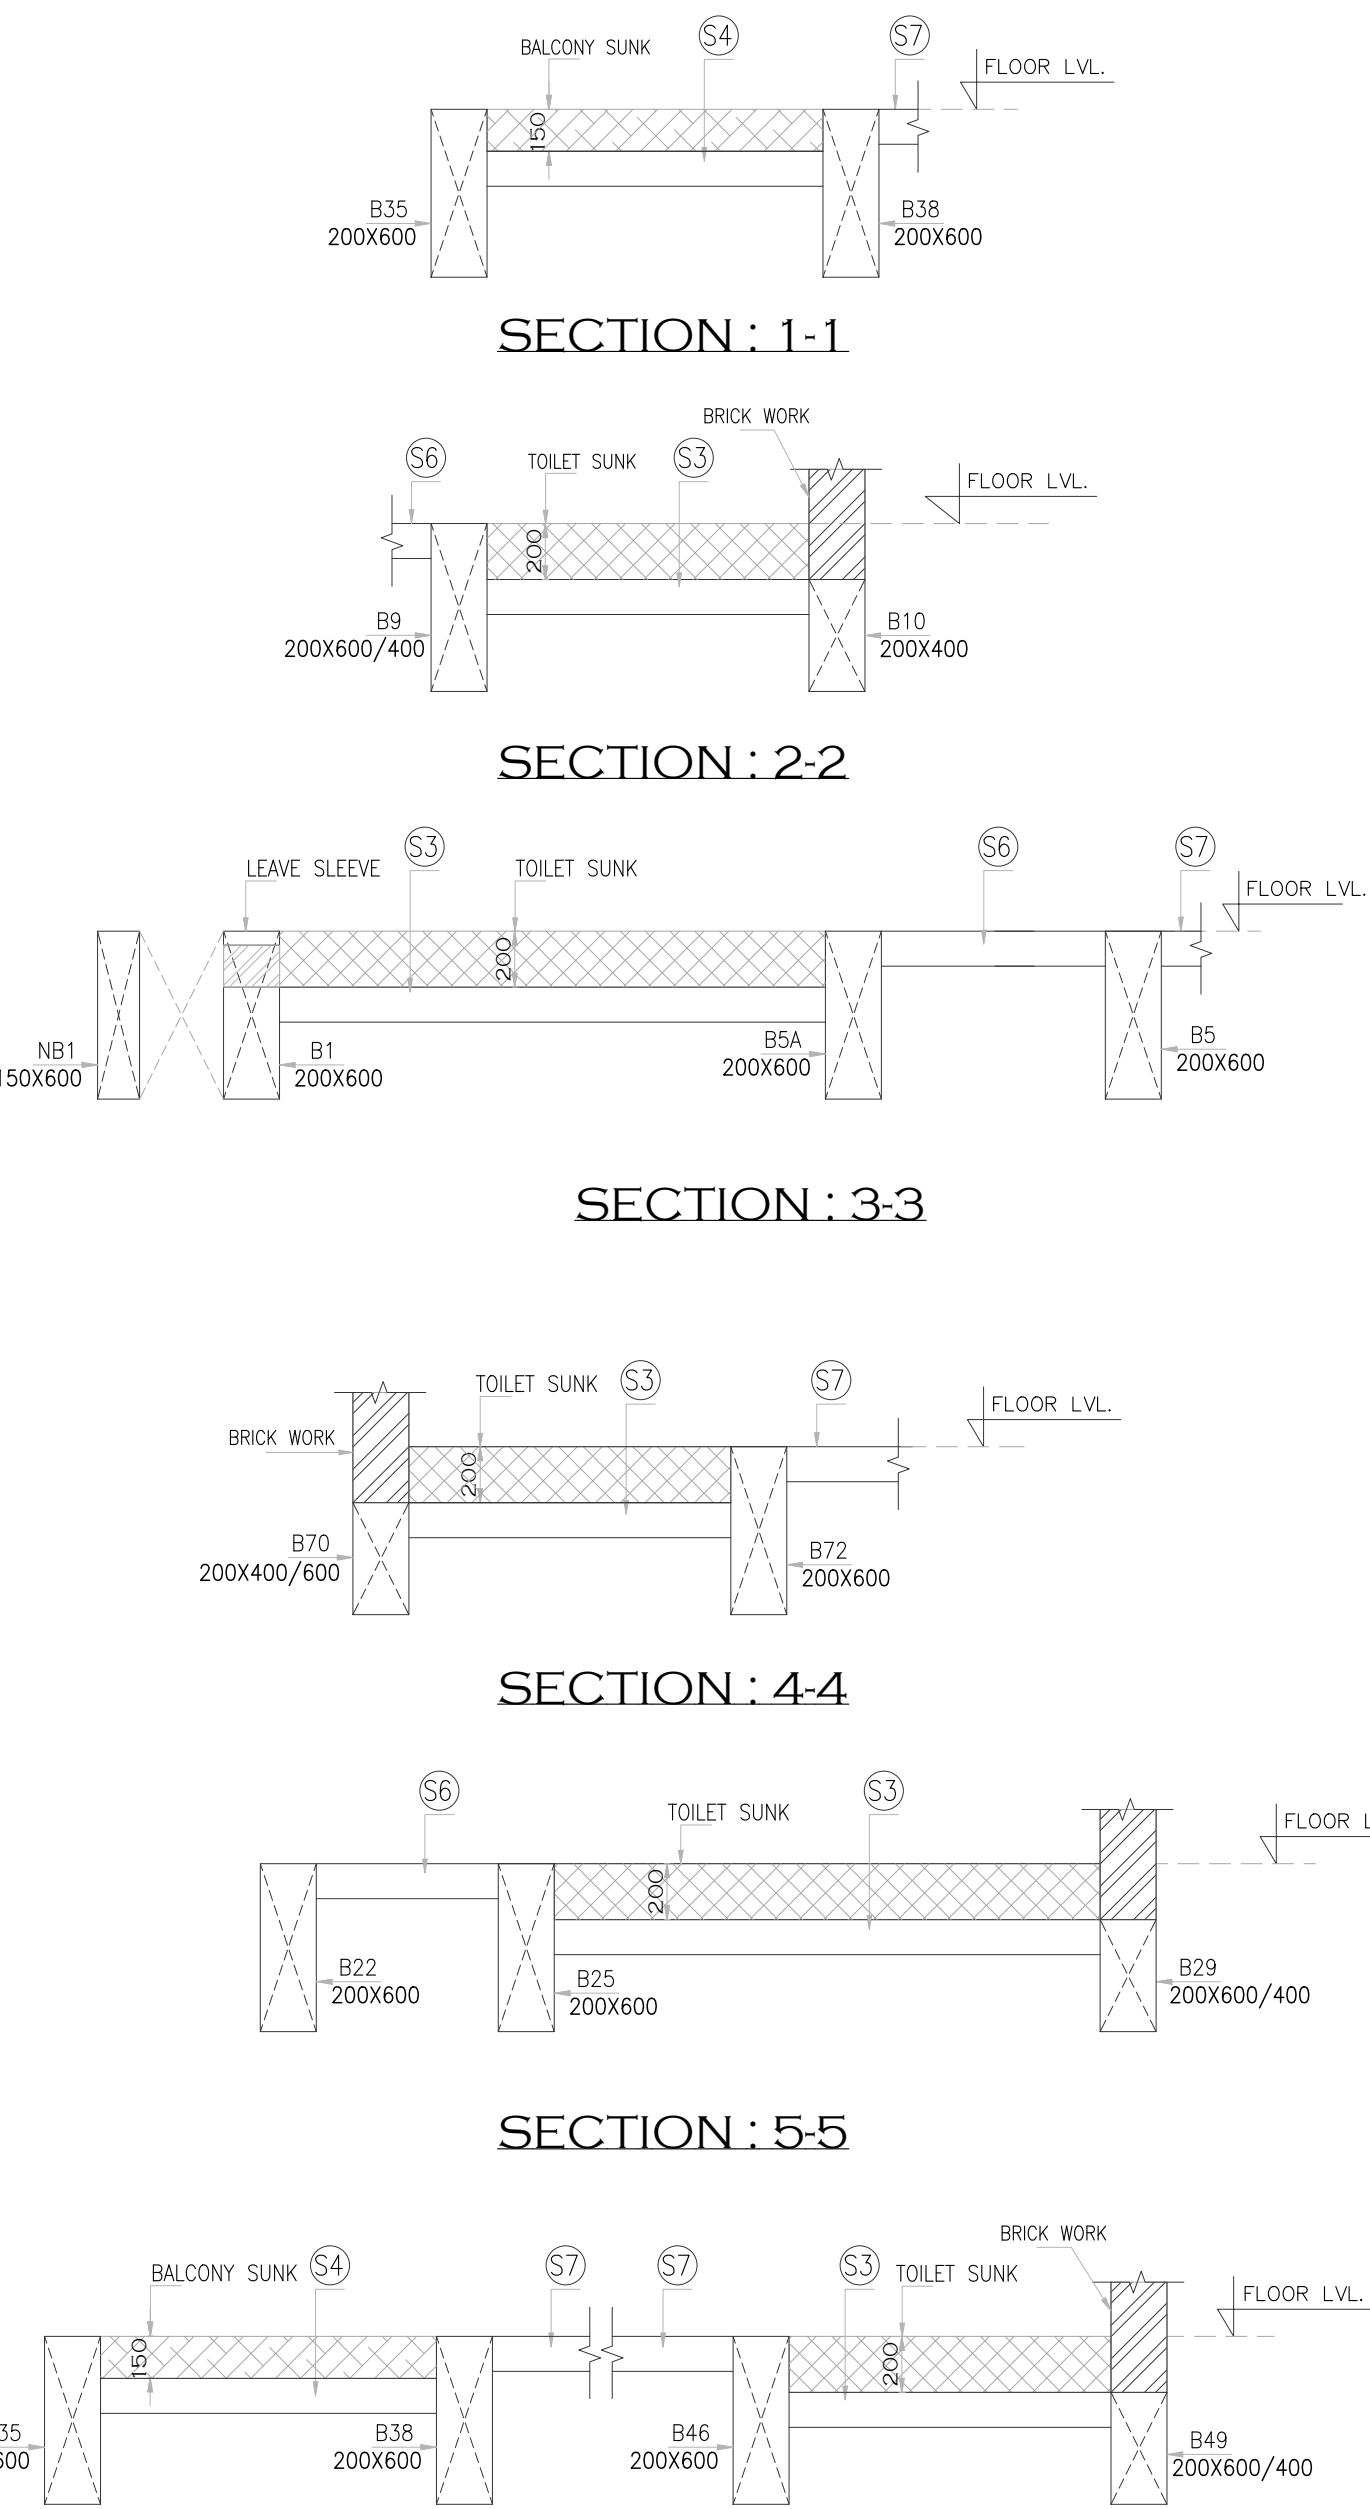

NOTES

REFER ARCHITECTURAL DRAWINGS PLAN, SECTION & ELEVATION.
ALONG WITH THIS DRAWING.

THIS DRAWING IS NOT TO BE SCALED.

BUILDING DESIGNED FOR STILT+7 FLOORS+
TERRACE FLOOR (NO PROVISION)


USE MIX M:30 & FE-500 STEEL

" T " INDICATES TOR STEEL

EXTERNAL & INTERNAL WALLS-RED BRICK

SC- 200X200+4T12 - STUB COLUMN

FOR SCHEDULE OF 2ND, 3RD & 4TH FLOOR REFER DRG. NO - 1293/BLDG-B/06A

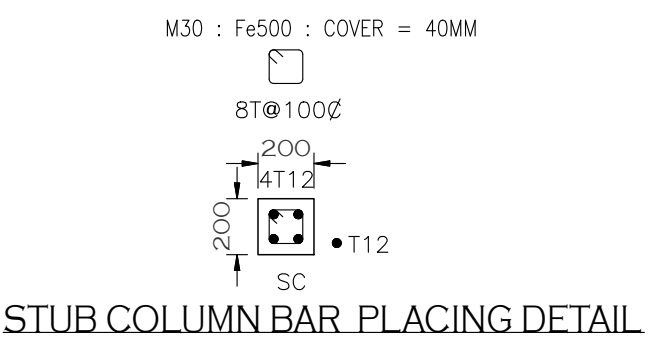

LEGENDS:-

200MM -TOILET SUNK

150MM-BALCONY SUNK

KEY PLAN

KEY SECTION

REVISION	DATE	DESCRIPTION	SIGN.
R2	02/07/2025	ADVANCE COPY	
R1	01/02/2025	REV.FOR COLUMN SIZES	
RO	25/12/2024	ADVANCE COPY	

DRG. TITLE :-
LAYOUT OF 2ND, 3RD & 4TH FLOOR.
(BLDG-B)

PROJECT:-
PPOPOSED RESIDENTIAL BILDING ON SR. NO. 49/2/2,
TALEGAON DABHADE, TAL:- MAVAL, DIST-PUNE

ARCHITECT:-
ARCH. SUHAS POL ,
TALEGAON DABHADE, TAL:- MAVAL, DIST-PUNE

CLIENT:-
M/S LANDSON DEVELOPERS

DRAWN BY :- SANDESH	CHECKED BY :- T.S.P.	SCALE :- 1:100
DRG. NO. 1293/BLDG-B/06	REVISION *R2	DATE 29/05/2024

THIS DRAWING IS THE PROPERTY AND COPYRIGHT OF
DESIGNAGE CONSULTANTS PRIVATE LIMITED
IT SHALL NOT BE COPIED OR REPRODUCED IN ANY MANNER WHATSOEVER AND
EXECUTED ON SITE SUBJECT TO APPROVAL OF COMPETENT AUTHORITY.



OFFICE NO-402, 4TH FLOOR ,WING-C
AUDUMBAR APARTMENTS CANAL ROAD,
NEAR VARDHMAN PETROL PUMP,WARJE,
PUNE, MAHARASHTRA -411052
Tel-9011076607, 9011016556
EMAIL - structure.pune@gmail.com
WEB SITE -www.designageconsultants.com